


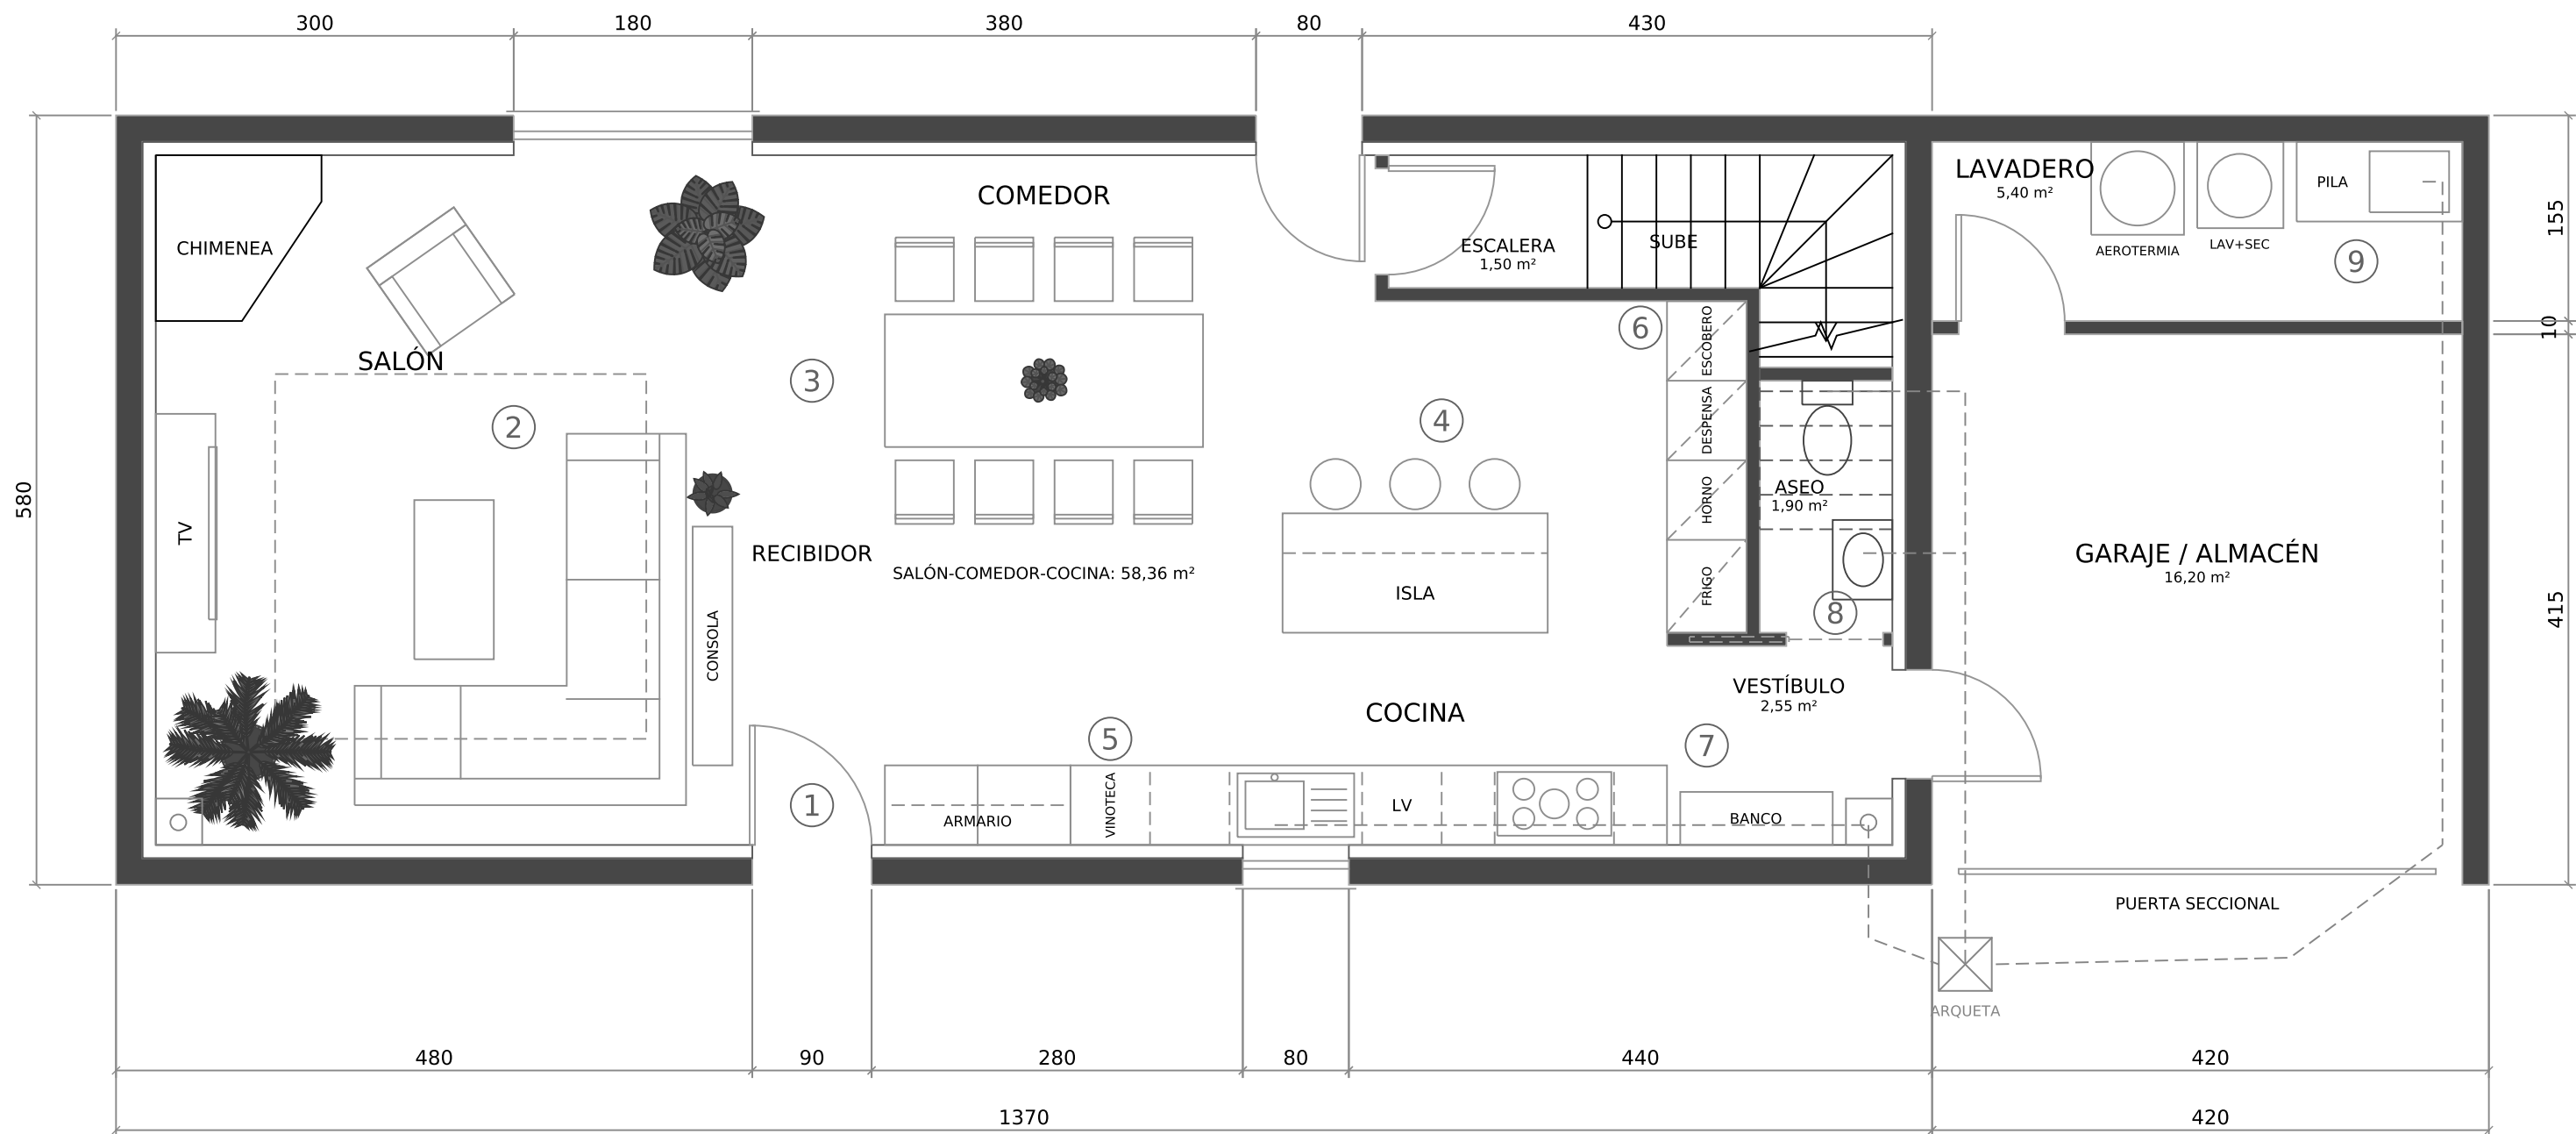

PLANTA BAJA - PROPUESTA OPTIMIZADA

Redibujada a partir de una captura: cotas aproximadas (escala estimada con el mobiliario). Ajustar con las medidas reales antes de usar.

- 1 Entrada: puerta abriendo hacia dentro, recibidor con armario 140x60 y consola que separa el salón.
- 2 Salón: sofá en L orientado a la TV (2,6 m) y butaca hacia la chimenea; paso libre de 1,3 m desde la entrada.
- 3 Comedor 8 plazas (240x100) separado 60 cm del muro trasero: antes las sillas quedaban pegadas a la pared.
- 4 Cocina en L + isla: fregadero bajo ventana, placa y columnas; pasillos de 90-100 cm; barra de 3 taburetes hacia el comedor.
- 5 Vinoteca bajo encimera en el extremo de la cocina más cercano al comedor.
- 6 Columnas de frigorífico, horno+micro, despensa y escobero en lugar de la despensa con puertas plegables.
- 7 Vestíbulo de servicio con banco: la puerta del garaje ya no choca con la encimera ni con la bajante (recomendado EI2 45-C5).
- 8 Aseo con puerta corredera empotrada al vestíbulo (en el plano original no tenía acceso).
- 9 Lavadero: lavadora+secadora en columna, pila con encimera y espacio de mantenimiento para la aerotermia.

Escalera existente sin cambios: comprobar número de peldaños y altura libre del aseo bajo el tramo superior.

Garaje: fondo útil aprox. 4,0 m (solo coche pequeño); comprobar con medidas reales.



ESCALA 1:50 en A3 - base de calco en grises